

KEY PLAN

NOTES:

THIS DRAWING MUST NOT BE SCALED.

ALL DIMENSIONS ARE TO BE VERIFIED AND CHECKED ON SITE. ANY DISCREPANCIES THAT ARE, OR BECOME APPARENT SHOULD BE REPORTED TO CHAPMAN TAYLOR.

AREAS INDICATED ARE APPROXIMATE GROSS INTERNAL AREA. THEY RELATE TO THE LIKELY AREAS OF THE BUILDING AT THE CURRENT STAGE OF DESIGN. ANY DECISIONS TO BE MADE ON THE BASIS OF THESE PREDICTIONS, WHETHER AS TO PROJECT VIABILITY, PRE-LETING, LEASE AGREEMENTS, OR THE LIKE, SHOULD INCLUDE DUE ALLOWANCE FOR THE INCREASES AND DECREASES INHERENT IN THE DESIGN DEVELOPMENT AND BUILDING PROCESS.

© COPYRIGHT CHAPMAN TAYLOR 2018

KEY:

- MEASURED APARTMENT AREA BOUNDARY
- PROPERTY LINE

AREAS OF STRUCTURE CLASH

SERVICES DRAINAGE:

- WI: WATER RISER
- EI: ELECTRICITY INCOMING
- RWO: RAIN WATER OUTLET
- RWP: RAIN WATER PIPE

RISERS:

- RWR: RAIN WATER RISER
- BCWS: BOOSTED COLD WATER SERVICE
- MSVS: MECHANICAL SMOKE VENTILATION SYSTEM
- LTHW: LOW TEMPERATURE HOT WATER
- LV: LOW VOLTAGE SUPPLY
- COMMS: COMMUNICATIONS
- CLR ST: CLEANER'S STORE

LEVELS:

- EGL: EXTERNAL GROUND LEVEL
- FFL: FINISHED FLOOR LEVEL
- FSL: FINISHED SLAB LEVEL
- FRL: FINISHED ROOF LEVEL
- TOP: TOP OF PARAPET LEVEL

|     |          |     |                                               |    |
|-----|----------|-----|-----------------------------------------------|----|
| C02 | 04/04/24 | JN  | INTERNAL DOORS - C02 ISSUE                    | SN |
| C01 | 16/01/24 | BM  | INTERNAL DOORS - C01 ISSUE                    | SN |
| P07 | 10/11/23 | APM | INTERNAL DOOR PACKAGE - P02                   | JK |
| P06 | 11/07/23 | BM  | MA COMMENTS INCORPORATED                      | SN |
| P05 | 12/12/22 | BM  | S2 - MA COMMENTS ON STAGE 3 PACK INCORPORATED | SN |
| P04 | 07/10/22 | BM  | VIP ISSUE FOR STAGE 3 REPORT                  | MW |
| P03 | 20/09/22 | APM | PRELIMINARY ISSUE - FOR COMMENT               | MW |
| P02 | 22/08/19 | CS  | PRELIMINARY ISSUE - FOR COMMENT               | MW |
| P01 | 22/08/05 | CS  | PRELIMINARY ISSUE                             | MW |

| REV | DATE | BY | DESCRIPTION | CHKD |
|-----|------|----|-------------|------|
|-----|------|----|-------------|------|

CLIENT



140 Aldersgate St,  
Barbican, London  
United Kingdom  
EC1A 4HT




Catalyst Housing, Ealing Gateway,  
26-30 Uxbridge Road, London  
United Kingdom  
W5 2AU

PROJECT

**Friary Park Phase 2**

Friary Road, Acton  
London, W3 6NL

ARCHITECT

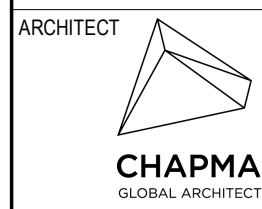

**CHAPMAN TAYLOR**  
GLOBAL ARCHITECTS & MASTERPLANNERS  
www.chapmantaylor.com

**LONDON STUDIO**  
30 Lambourne Terrace  
London W2 6LG  
United Kingdom  
T +44 (0)20 7571 3000  
E london@chapmantaylor.com

STRUCTURAL ENGINEER



**PATRICK PARSONS**

34 Candler Meads  
Ainslie Park Road  
Twickenham, London  
United Kingdom  
TW1 3JF

SERVICES ENGINEER



**AECOM**

AECOM House  
Home Lane, Bedford  
United Kingdom  
MK40 1TS

LANDSCAPE ARCHITECT



**EXTERIOR  
ARCHITECTURE**

THE LEATHER MARKET Unit 17.1  
11-13 Weston St, London  
United Kingdom  
SE1 3ER

DRAWING TITLE


**BLOCK E, LEVEL 02  
GENERAL ARRANGEMENT PLAN**

|       |              |
|-------|--------------|
| Scale | 1 : 100 @ A1 |
|-------|--------------|

|                 |   |            |   |          |            |          |        |
|-----------------|---|------------|---|----------|------------|----------|--------|
| INTERNAL JOB NO | 1 | ISSUE DATE | 5 | DRAWN BY | CHECKED BY | CATEGORY | STATUS |
|-----------------|---|------------|---|----------|------------|----------|--------|

|         |          |     |    |    |    |  |  |
|---------|----------|-----|----|----|----|--|--|
| C049FPP | 18/10/22 | APM | MW | 04 | S4 |  |  |
|---------|----------|-----|----|----|----|--|--|

|                |        |            |     |    |    |   |        |          |     |
|----------------|--------|------------|-----|----|----|---|--------|----------|-----|
| PROJECT NUMBER | W36002 | ORIGINATOR | CTA | EE | 02 | D | A00003 | REVISION | C02 |
|----------------|--------|------------|-----|----|----|---|--------|----------|-----|

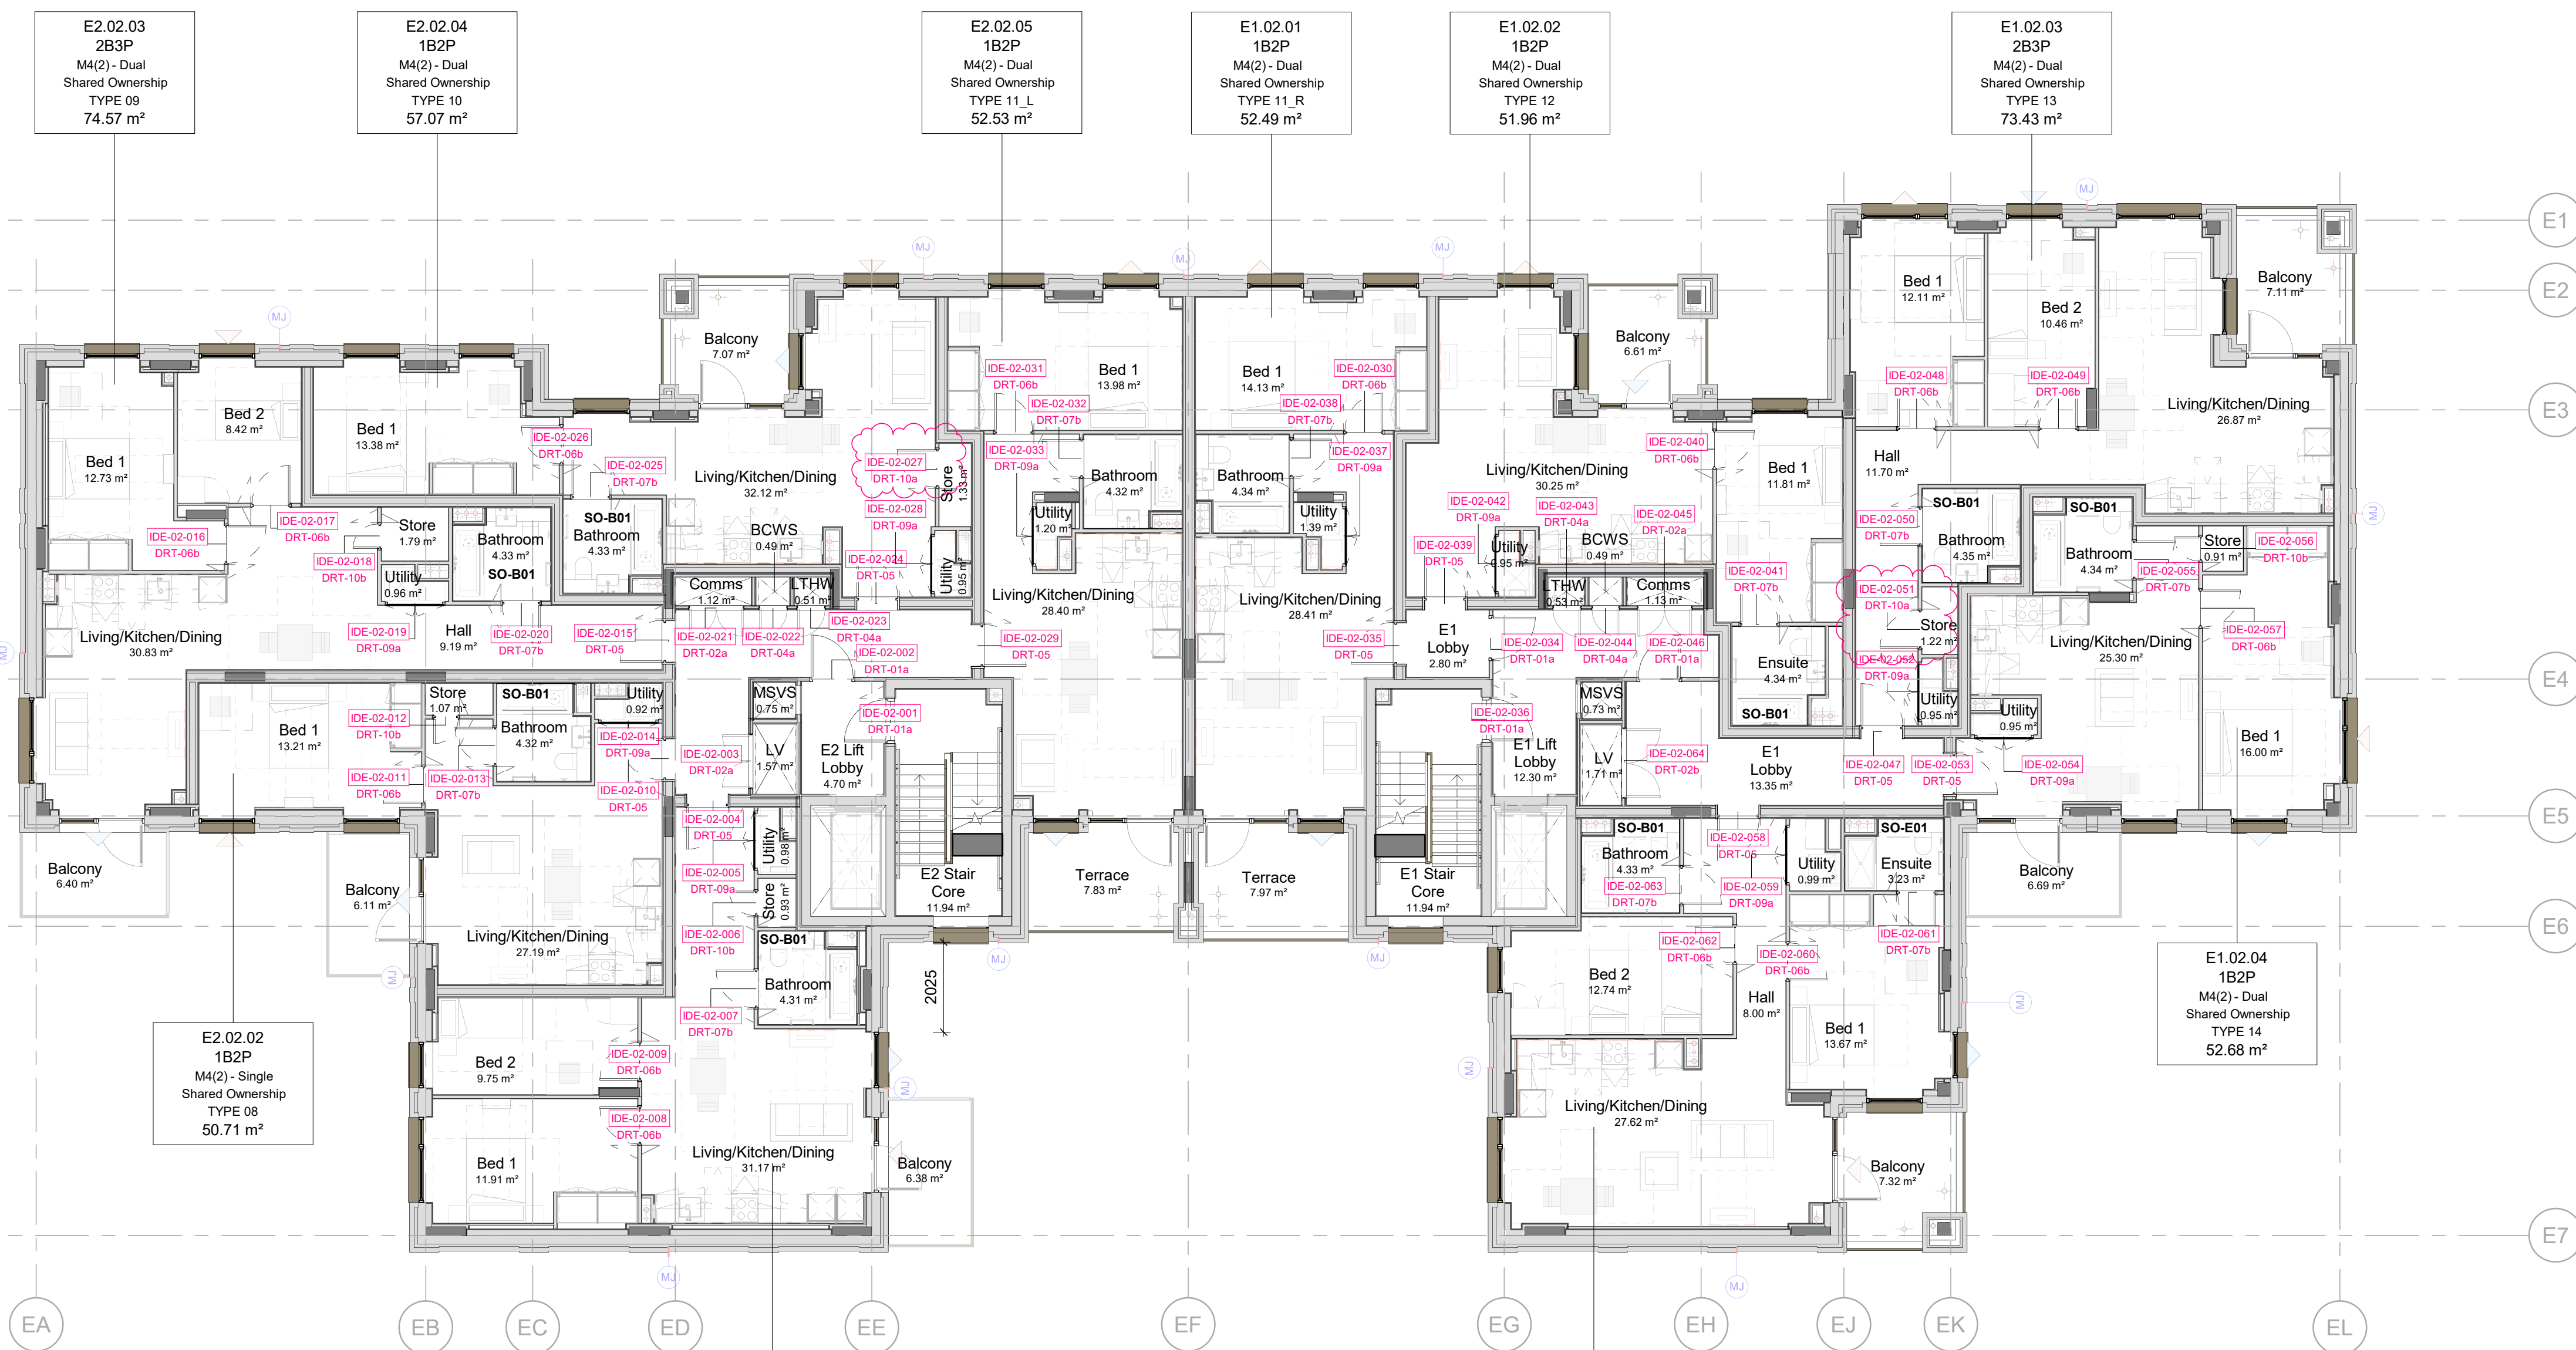

1 GENERAL ARRANGEMENT - L02

1 : 100