

KEY PLAN

NOTES:

THIS DRAWING MUST NOT BE SCALED.
ALL DIMENSIONS ARE TO BE VERIFIED AND CHECKED ON SITE. ANY DISCREPANCIES THAT ARE, OR BECOME APPARENT SHOULD BE REPORTED TO CHAPMAN TAYLOR.
AREAS INDICATED ARE APPROXIMATE GROSS INTERNAL AREA. THEY RELATE TO THE LIKELY AREAS OF THE BUILDING AT THE CURRENT STAGE OF DESIGN. ANY DECISIONS TO BE MADE ON THE BASIS OF THESE PREDICTIONS, WHETHER AS TO PROJECT VIABILITY, PRE-LETTING, LEASE AGREEMENTS, OR THE LIKE, SHOULD INCLUDE DUE ALLOWANCE FOR THE INCREASES AND DECREASES INHERENT IN THE DESIGN DEVELOPMENT AND BUILDING PROCESS.

© COPYRIGHT CHAPMAN TAYLOR 2018

KEY:

MEASURED APARTMENT
AREA BOUNDARY
PROPERTY LINE

AREAS OF STRUCTURE
CLASH

SERVICES DRAINAGE:

WI: WATER RISER
EI: ELECTRICITY INCOMING
RWO: RAIN WATER OUTLET
RWP: RAIN WATER PIPE

RISERS:

RWR: RAIN WATER RISER
BCWS: BOOSTED COLD WATER SERVICE
MSVS: MECHANICAL SMOKE VENTILATION SYSTEM
LTHW: LOW TEMPERATURE HOT WATER
LV: LOW VOLTAGE SUPPLY
COMMS: COMMUNICATIONS
CLR ST: CLEANER'S STORE

LEVELS:

EGL: EXTERNAL GROUND LEVEL
FFL: FINISHED FLOOR LEVEL
FSL: FINISHED SLAB LEVEL
FRL: FINISHED ROOF LEVEL
TOP: TOP OF PARAPET LEVEL

C02	04/04/24	JN	INTERNAL DOORS - C02 ISSUE	SN
C01	16/01/24	BM	INTERNAL DOORS - C01 ISSUE	SN
P07	10/11/23	APM	INTERNAL DOOR PACKAGE - P02	JK
P06	11/07/23	BM	IA COMMENTS INCORPORATED	SN
P05	12/12/22	BM	S2 - IA COMMENTS ON STAGE 3 PACK INCORPORATED	SN
P04	07/10/22	BM	VIIP ISSUE FOR STAGE 3 REPORT	MW
P03	20/09/22	APM	PRELIMINARY ISSUE - FOR COMMENT	MW
P02	22/08/19	CS	PRELIMINARY ISSUE - FOR COMMENT	MW
P01	22/08/05	CS	PRELIMINARY ISSUE	MW

REV	DATE	BY	DESCRIPTION	CHKD
-----	------	----	-------------	------

CLIENT



140 Aldersgate St.
Barbican, London
United Kingdom
EC1A 4RY




Catalyst Housing, Ealing Gateway,
26-30 Uxbridge Road, London
United Kingdom
W5 2AU

PROJECT

Friary Park Phase 2
Friary Road, Acton
London, W3 6NL

ARCHITECT

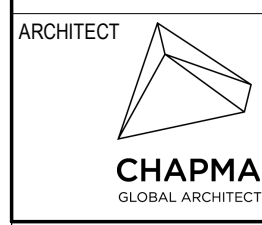

CHAPMAN TAYLOR
GLOBAL ARCHITECTS & MASTERPLANNERS

LONDON STUDIO
30 Lambourne Terrace
London W2 6LG
United Kingdom
T +44 (0)20 7571 3000
E london@chapmantaylor.com
www.chapmantaylor.com

STRUCTURAL ENGINEER



PATRICK PARSONS

34 Candler Meads
Amarynd Park Road
Twickenham, London
United Kingdom
TW1 3JF

SERVICES ENGINEER



AECOM

AECOM House
Home Lane, Bedford
United Kingdom
MK40 1TS

LANDSCAPE ARCHITECT




**EXTERIOR
ARCHITECTURE**

THE LEATHER MARKET Unit 17.1
11-13 Weston St, London
United Kingdom
SE1 3ER

DRAWING TITLE

**BLOCK E, LEVEL 03
GENERAL ARRANGEMENT PLAN**

Scale 1 : 100 @ A1		1		5		10M	
INTERNAL JOB NO	ISSUE DATE	DRAWN BY	CHECKED BY	CATEGORY	STATUS		
C049FPP	18/10/22	APM	MW	04	S4		
PROJECT NUMBER	ORIGINATOR	FUNC. BRK.	SP. BRK.	FORM.	DEC.	NUMBER	REVISION
W36002	CTA	EE	03	D	A	00004	C02

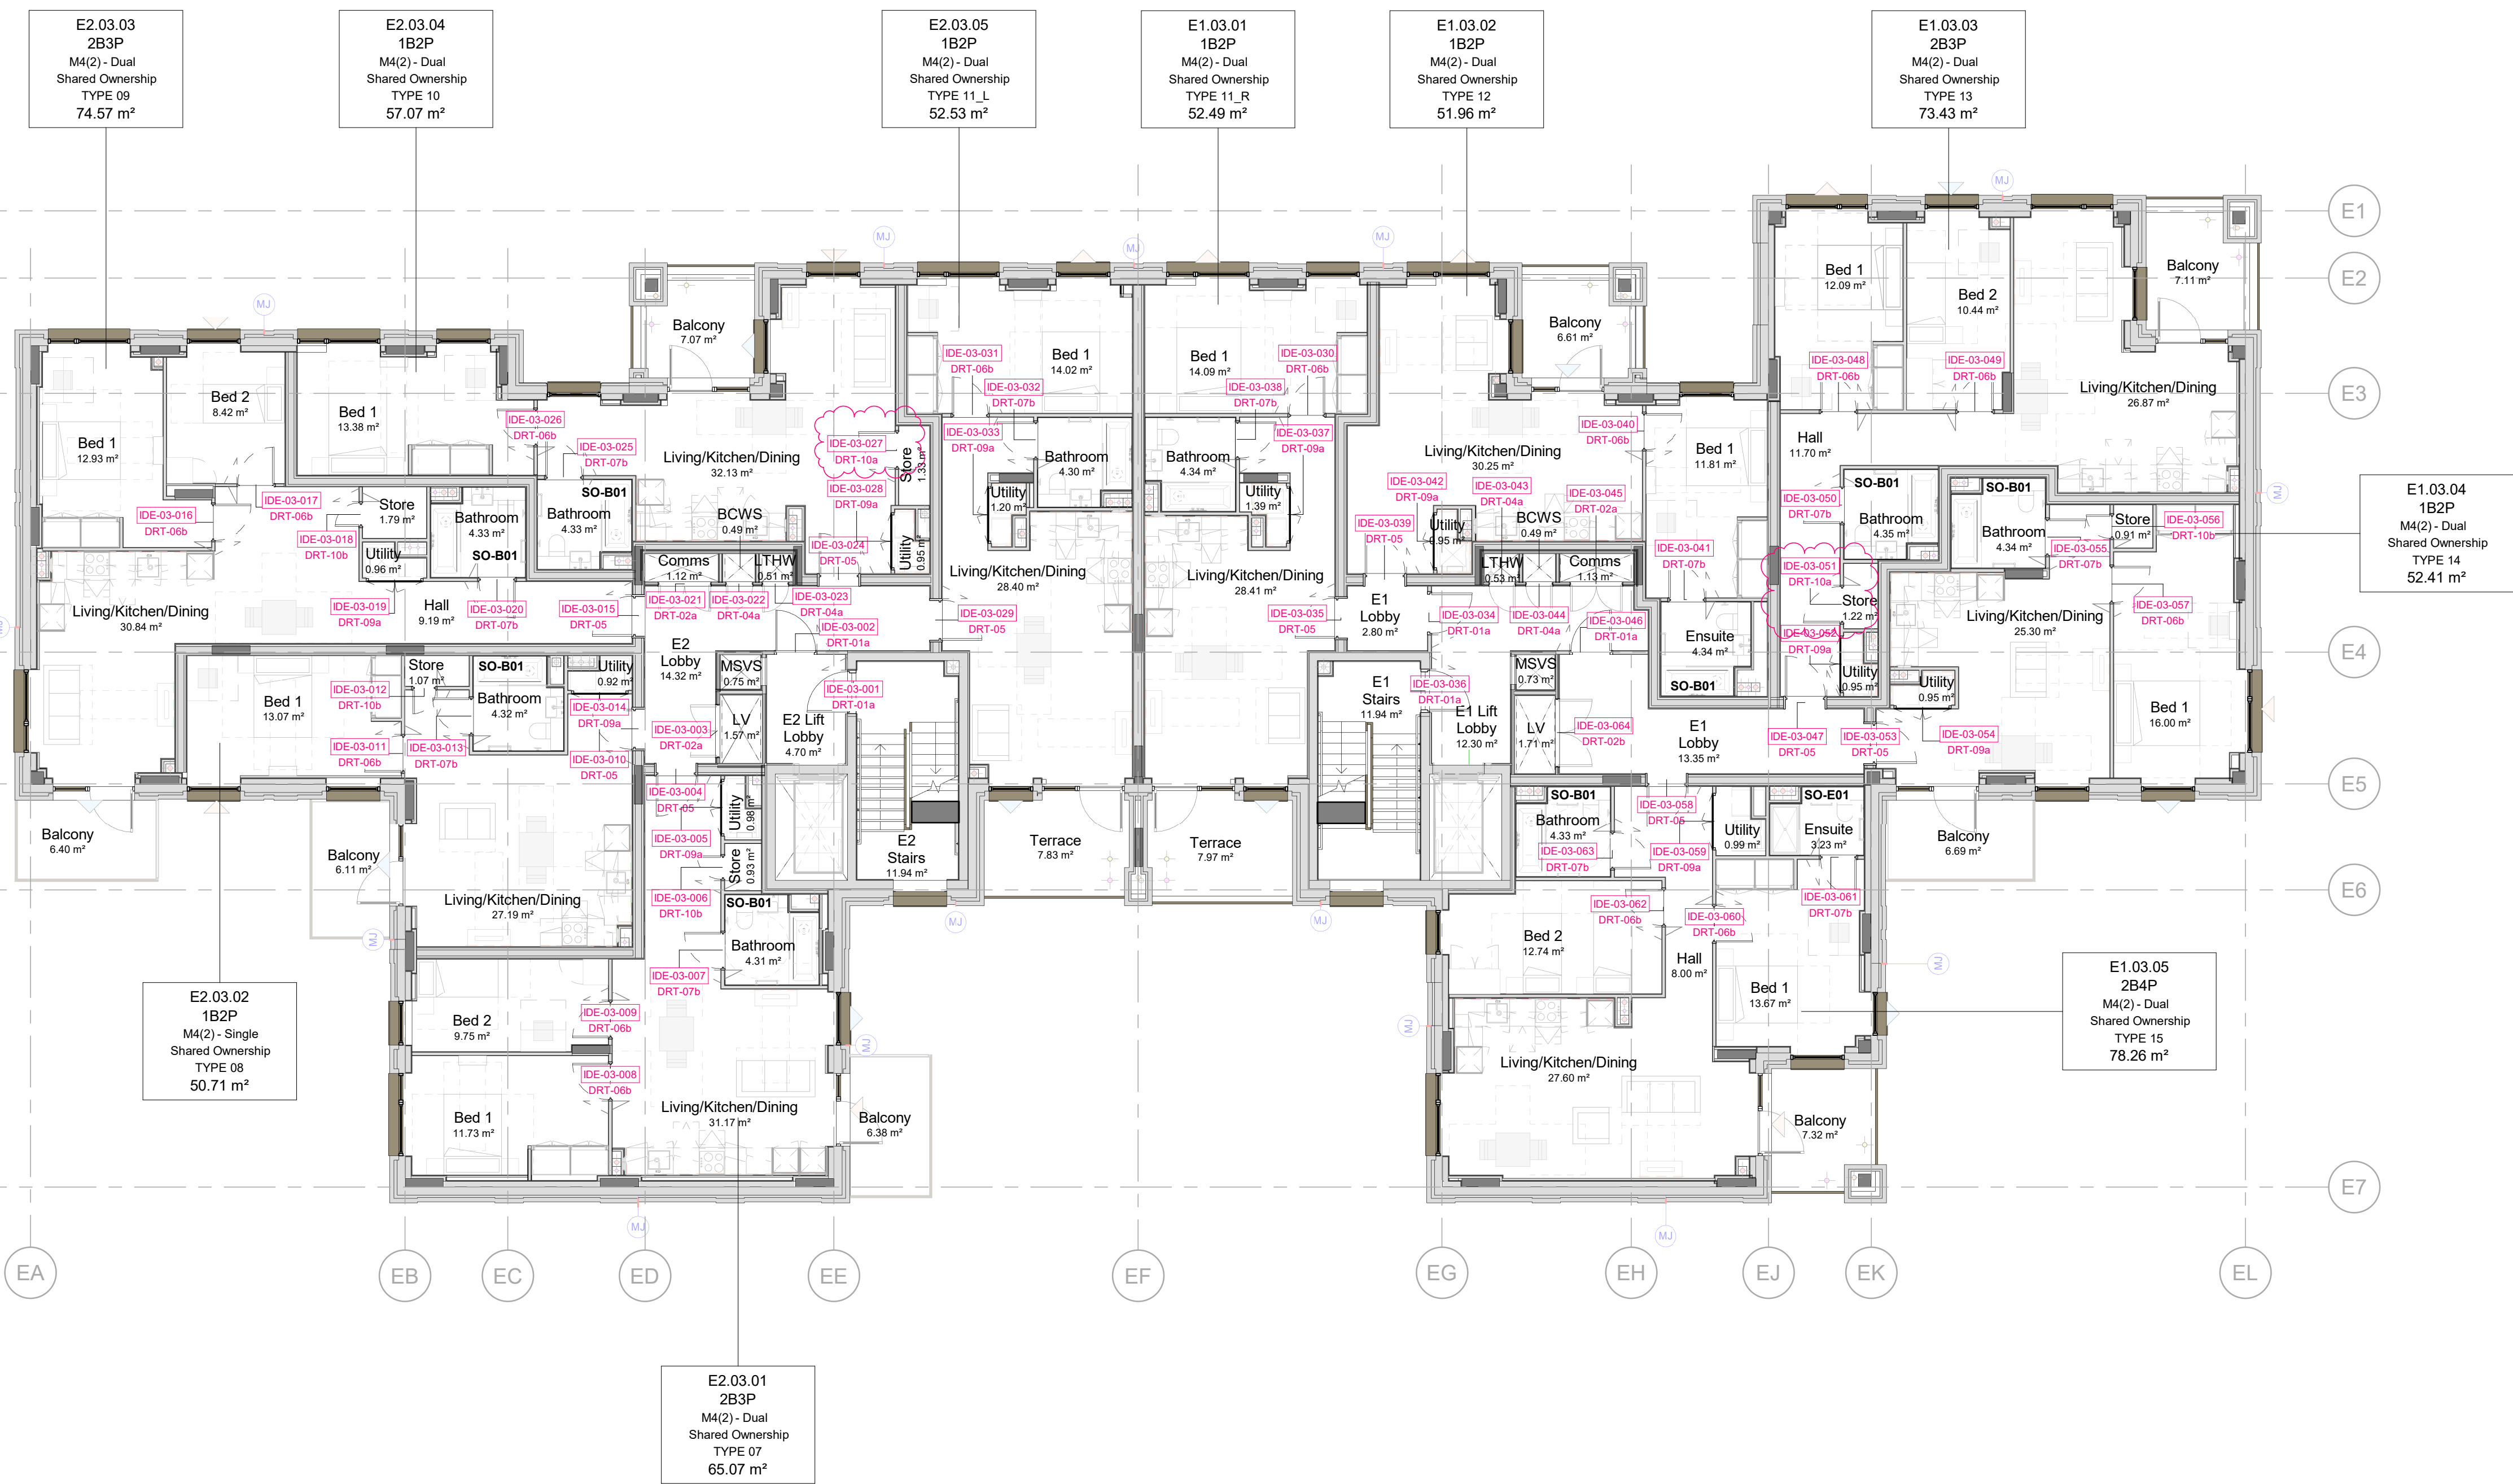

1 GENERAL ARRANGEMENT - L03
1 : 100