

KEY PLAN

NOTES:

THIS DRAWING MUST NOT BE SCALED.
ALL DIMENSIONS ARE TO BE VERIFIED AND CHECKED ON SITE. ANY DISCREPANCIES THAT ARE, OR BECOME APPARENT SHOULD BE REPORTED TO CHAPMAN TAYLOR.
AREAS INDICATED ARE APPROXIMATE GROSS INTERNAL AREA. THEY RELATE TO THE LIKELY AREAS OF THE BUILDING AT THE CURRENT STAGE OF DESIGN. ANY DECISIONS TO BE MADE ON THE BASIS OF THESE PREDICTIONS, WHETHER AS TO PROJECT VIABILITY, PRE-LETING, LEASE AGREEMENTS, OR THE LIKE, SHOULD INCLUDE DUE ALLOWANCE FOR THE INCREASES AND DECREASES INHERENT IN THE DESIGN DEVELOPMENT AND BUILDING PROCESS.

© COPYRIGHT CHAPMAN TAYLOR 2018

KEY:

- MEASURED APARTMENT AREA BOUNDARY
- PROPERTY LINE

AREAS OF STRUCTURE CLASH

SERVICES DRAINAGE:

- WI: WATER RISER
- EI: ELECTRICITY INCOMING
- RWO: RAIN WATER OUTLET
- RWP: RAIN WATER PIPE

RISERS:

- RWR: RAIN WATER RISER
- BCWS: BOOSTED COLD WATER SERVICE
- MSVS: MECHANICAL SMOKE VENTILATION SYSTEM
- LTHW: LOW TEMPERATURE HOT WATER
- LV: LOW VOLTAGE SUPPLY
- COMMS: COMMUNICATIONS
- CLR ST: CLEANER'S STORE

LEVELS:

- EGL: EXTERNAL GROUND LEVEL
- FFL: FINISHED FLOOR LEVEL
- FSL: FINISHED SLAB LEVEL
- FRL: FINISHED ROOF LEVEL
- TOP: TOP OF PARAPET LEVEL

C02	04/04/24	JN	INTERNAL DOORS - C02 ISSUE	SN
C01	16/01/24	BM	INTERNAL DOORS - C01 ISSUE	SN
P07	10/11/23	APM	INTERNAL DOOR PACKAGE - P02	JK
P06	11/07/23	BM	IA COMMENTS INCORPORATED	SN
P05	12/12/22	BM	S2 - IA COMMENTS ON STAGE 3 PACK INCORPORATED	SN
P04	07/10/22	BM	VIP ISSUE FOR STAGE 3 REPORT	MW
P03	20/09/22	APM	PRELIMINARY ISSUE - FOR COMMENT	MW
P02	22/08/19	CS	PRELIMINARY ISSUE - FOR COMMENT	MW
P01	22/08/05	CS	PRELIMINARY ISSUE	MW

REV	DATE	BY	DESCRIPTION	CHKD
-----	------	----	-------------	------

140 Aldersgate St.
Barbican, London
United Kingdom
EC1A 4HY

Catalyst Housing, Ealing Gateway,
26-30 Uxbridge Road, London
United Kingdom
W5 2AU

PROJECT

Friary Park Phase 2
Friary Road, Acton
London, W3 6NL

CHAPMAN TAYLOR
GLOBAL ARCHITECTS & INTERIORS

LONDON STUDIO
30 Lambourne Terrace
London W2 6LG
United Kingdom
T +44 (0)20 7371 3000
E london@chapmantaylor.com
www.chapmantaylor.com

STRUCTURAL ENGINEER

34 Candler Mews
Amarynd Park Road
Twickenham, London
United Kingdom
TW1 3JF

SERVICES ENGINEER


AECOM House
Home Lane, Bedford
United Kingdom
MK40 1TS

LANDSCAPE ARCHITECT

THE LEATHER MARKET Unit 17.1
11-13 Weston St, London
United Kingdom
SE1 3ER

DRAWING TITLE
BLOCK E, LEVEL 04
GENERAL ARRANGEMENT PLAN

Scale 1 : 100 @ A1		1		5		10M	
INTERNAL JOB NO	ISSUE DATE	DRAWN BY	CHECKED BY	CATEGORY	STATUS		
C049FPP	18/10/22	APM	MW	04	S4		
PROJECT NUMBER	ORIGINATOR	FUNC. BRK	SP. BRK	FORM	DEC. NUMBER	REVISION	
W36002	CTA	EE	04	D	A 00005	C02	

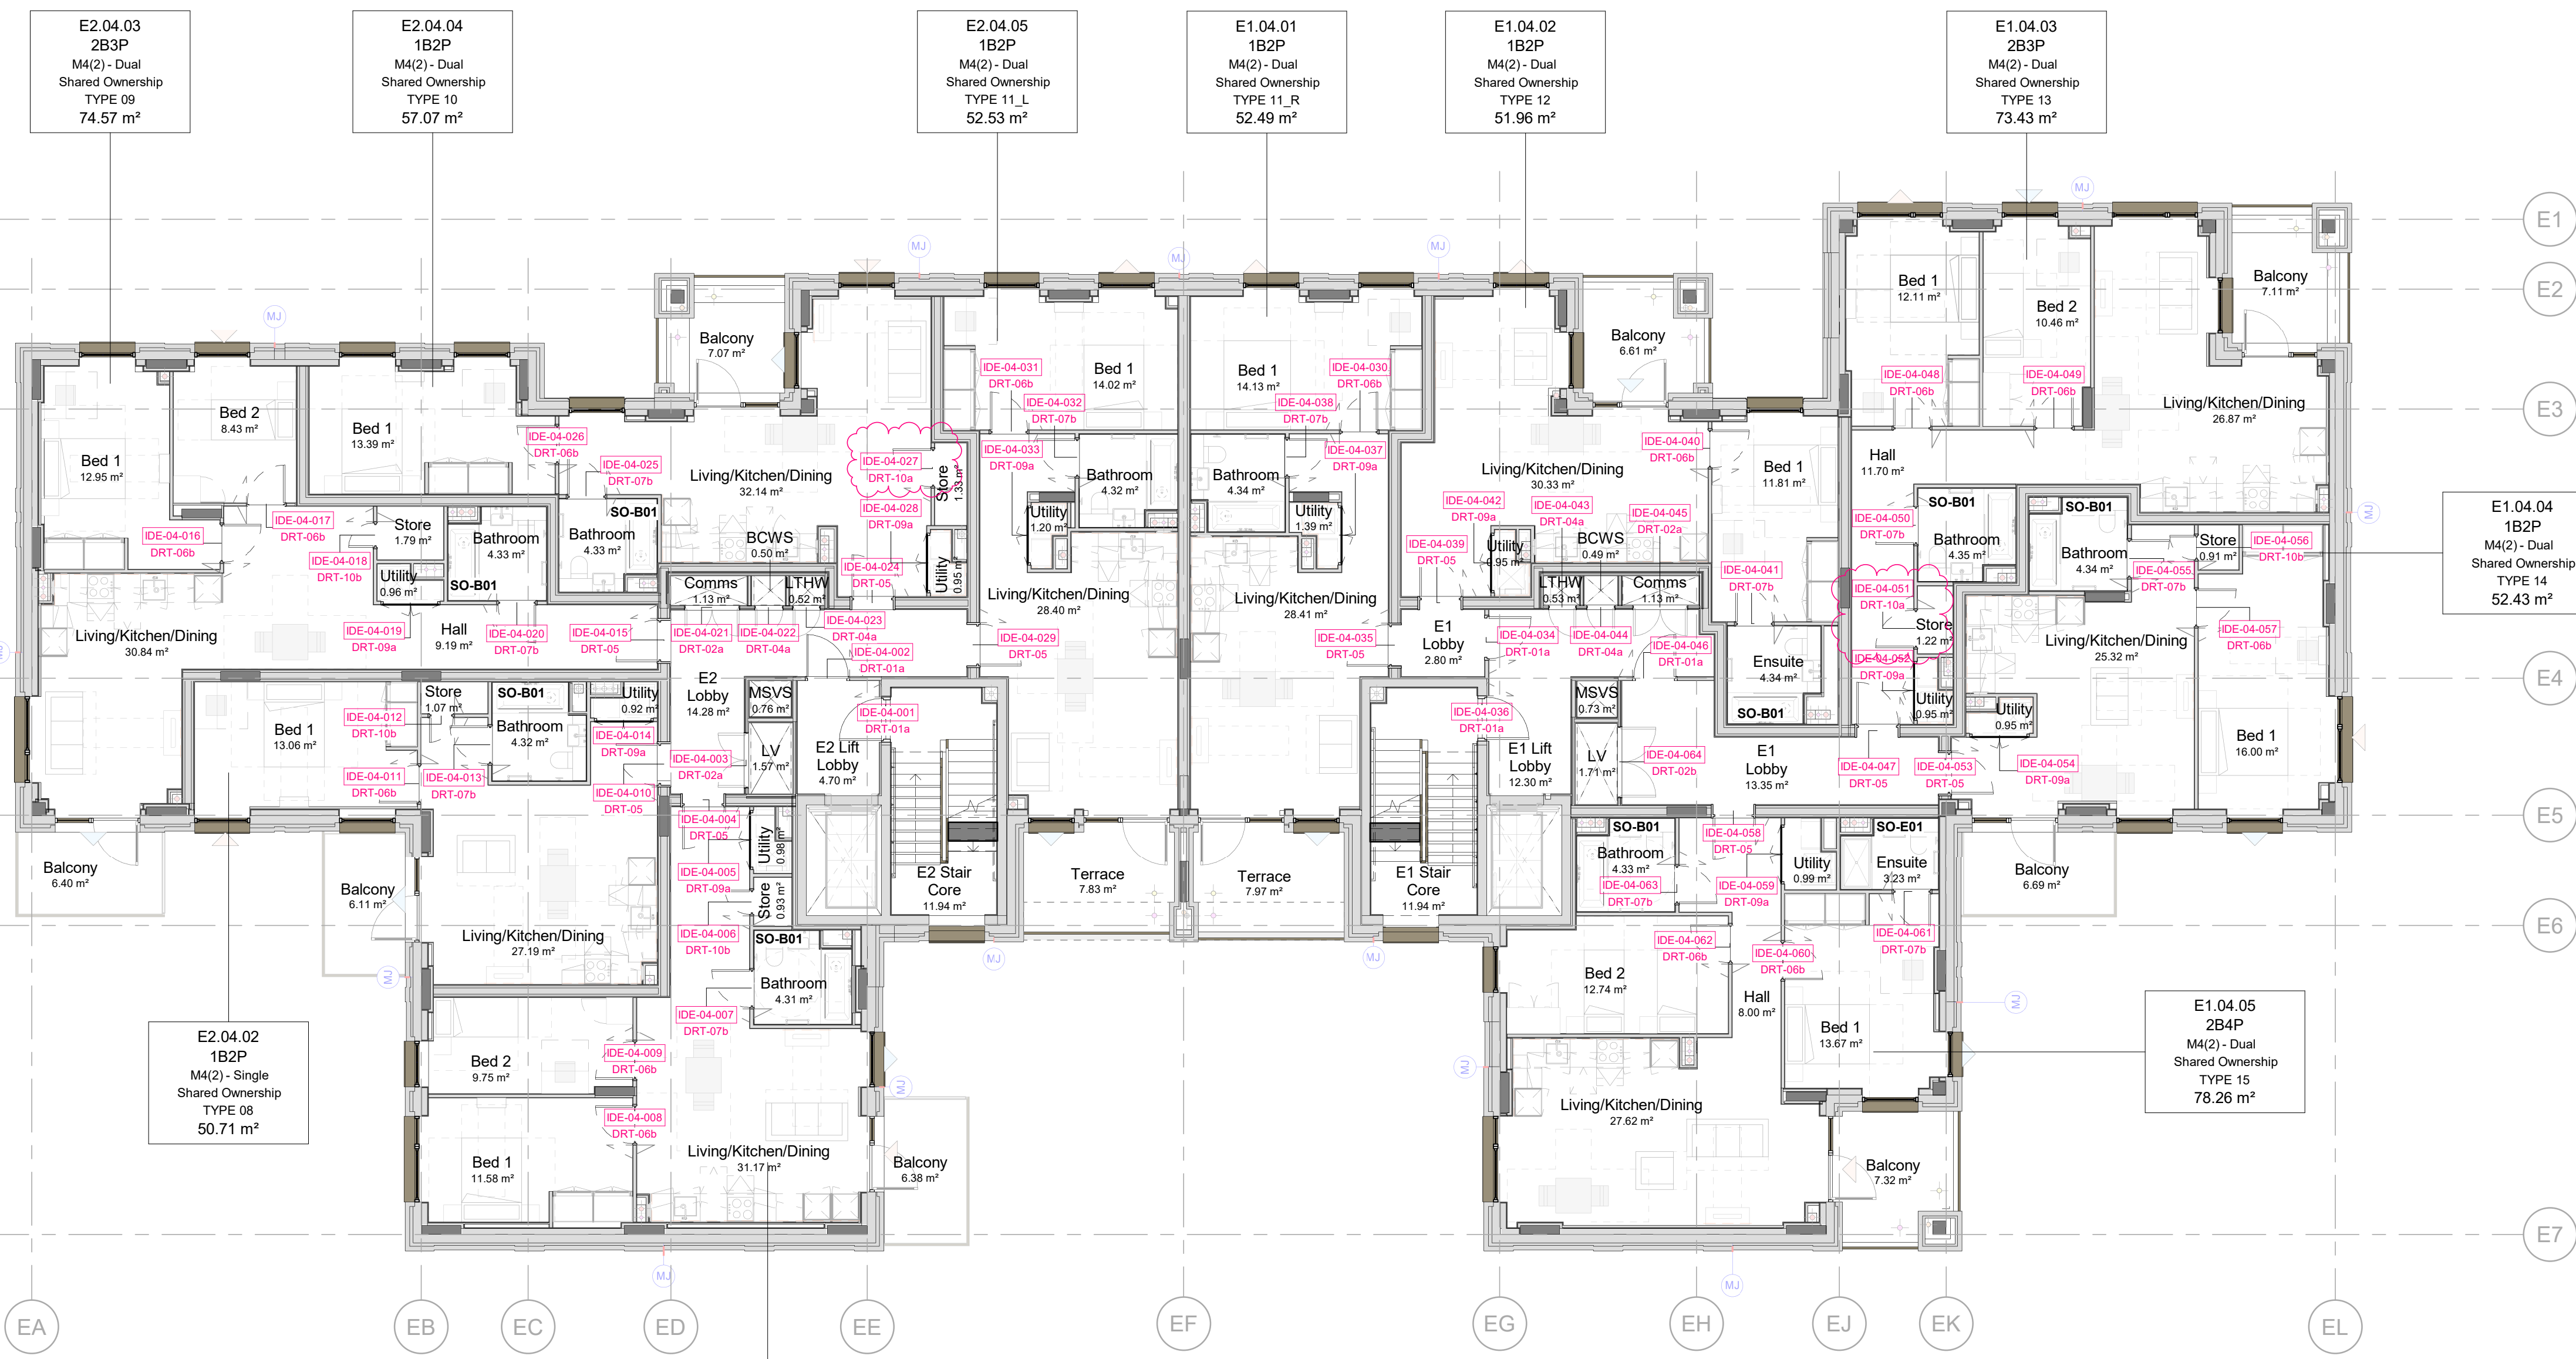

1 GENERAL ARRANGEMENT - L04
1 : 100